


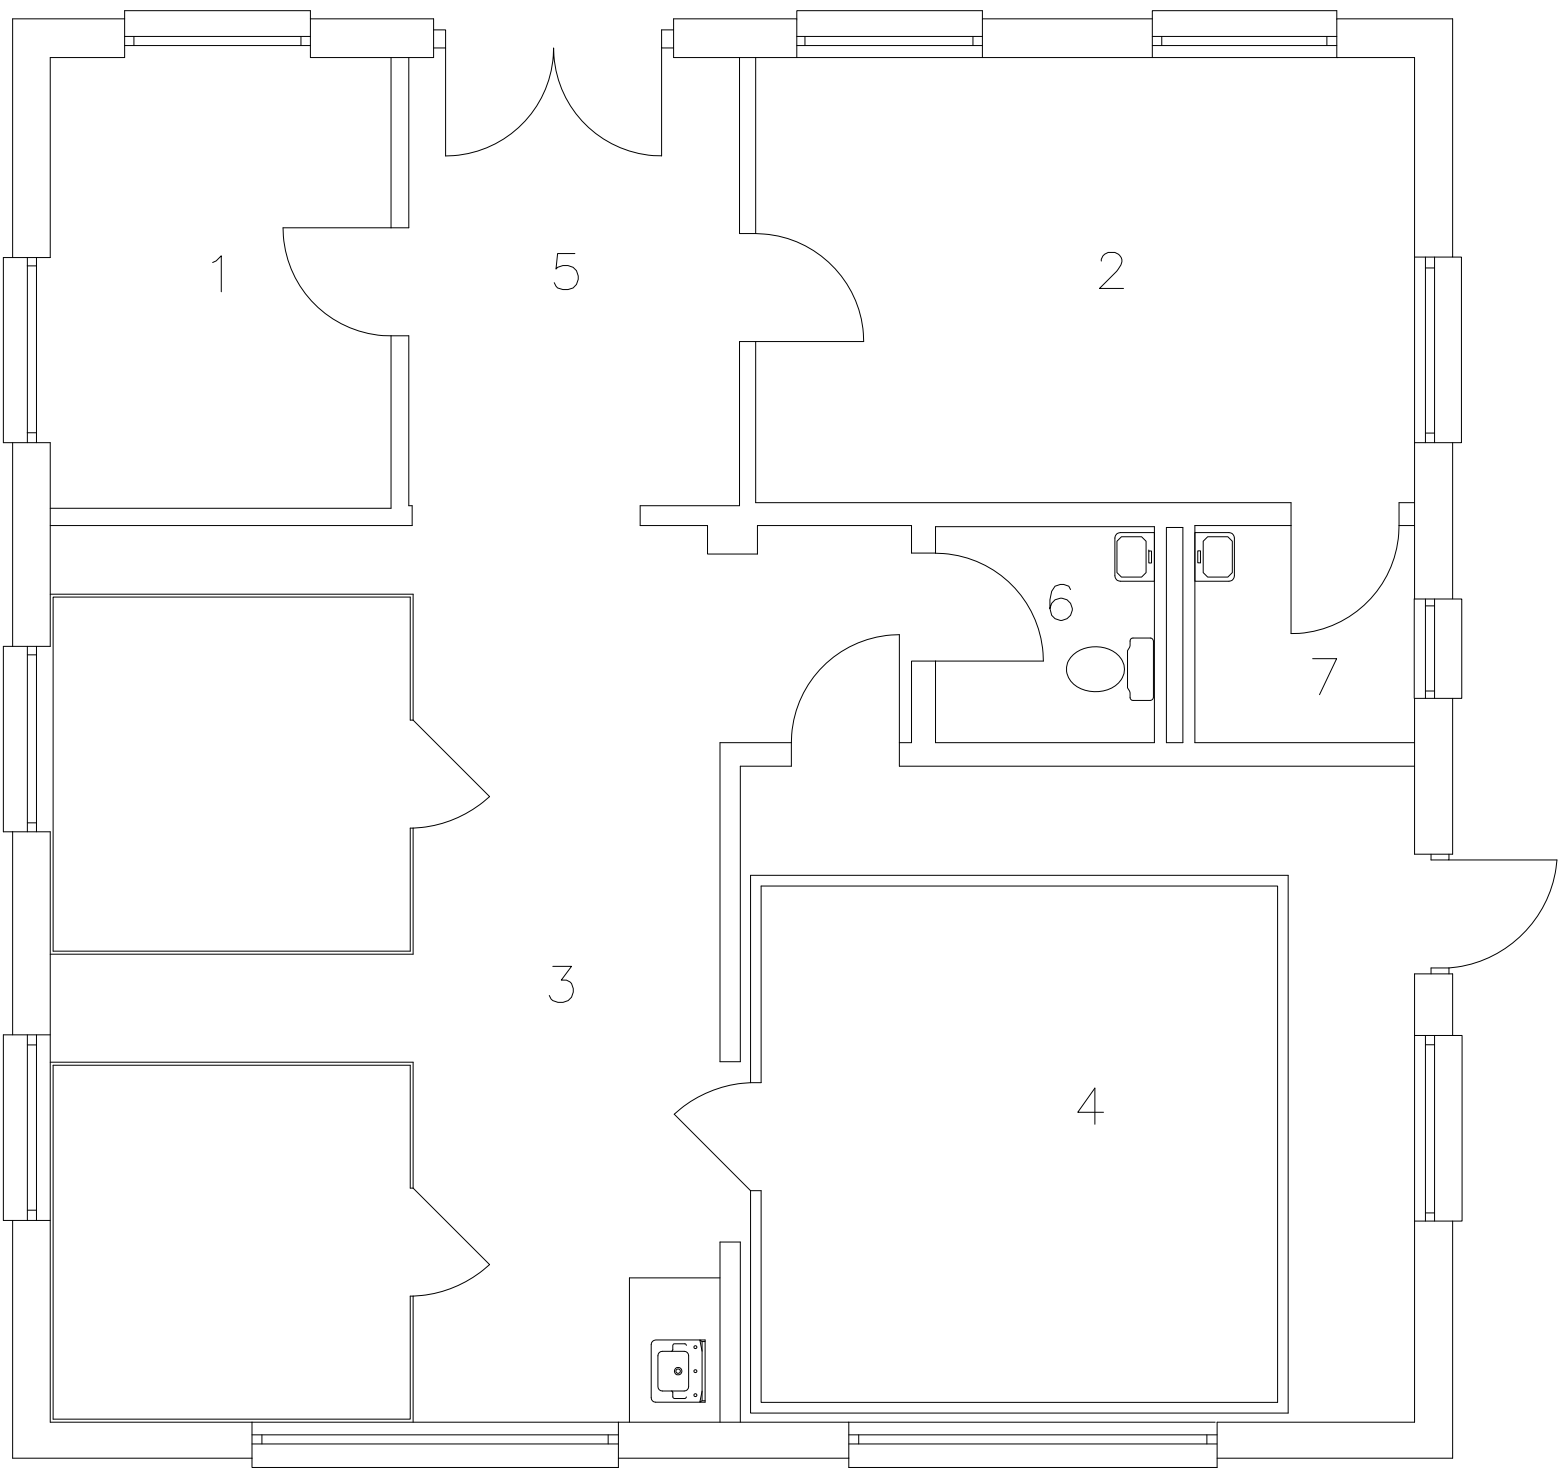

The University of Texas at Austin


space@austin.utexas.edu

CMRG CONCRETE DURABIL. CTR.(PRC 26)

CM2 (0937)

FLOOR: FIRST (01)

DATE: 6/1/2015

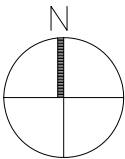

SCALE: 3/16" = 1'-0"